




Orientação

NG
NM
Sistema de Coordenadas
Projeção UTM
referenciadas ao Meridiano
Central -51
Fuso 23S
DATUM SIRGAS 2000


Convergência e declinação do vértice: P0
Convergência Meridiana: -0.06339105673322042
Latitude: 9841705.030
Longitude: 114796.448
Data: 11/02/2023

Convenções Topográficas

- Ruas
- Calçadas
- Vértices
- ▨ Confinantes

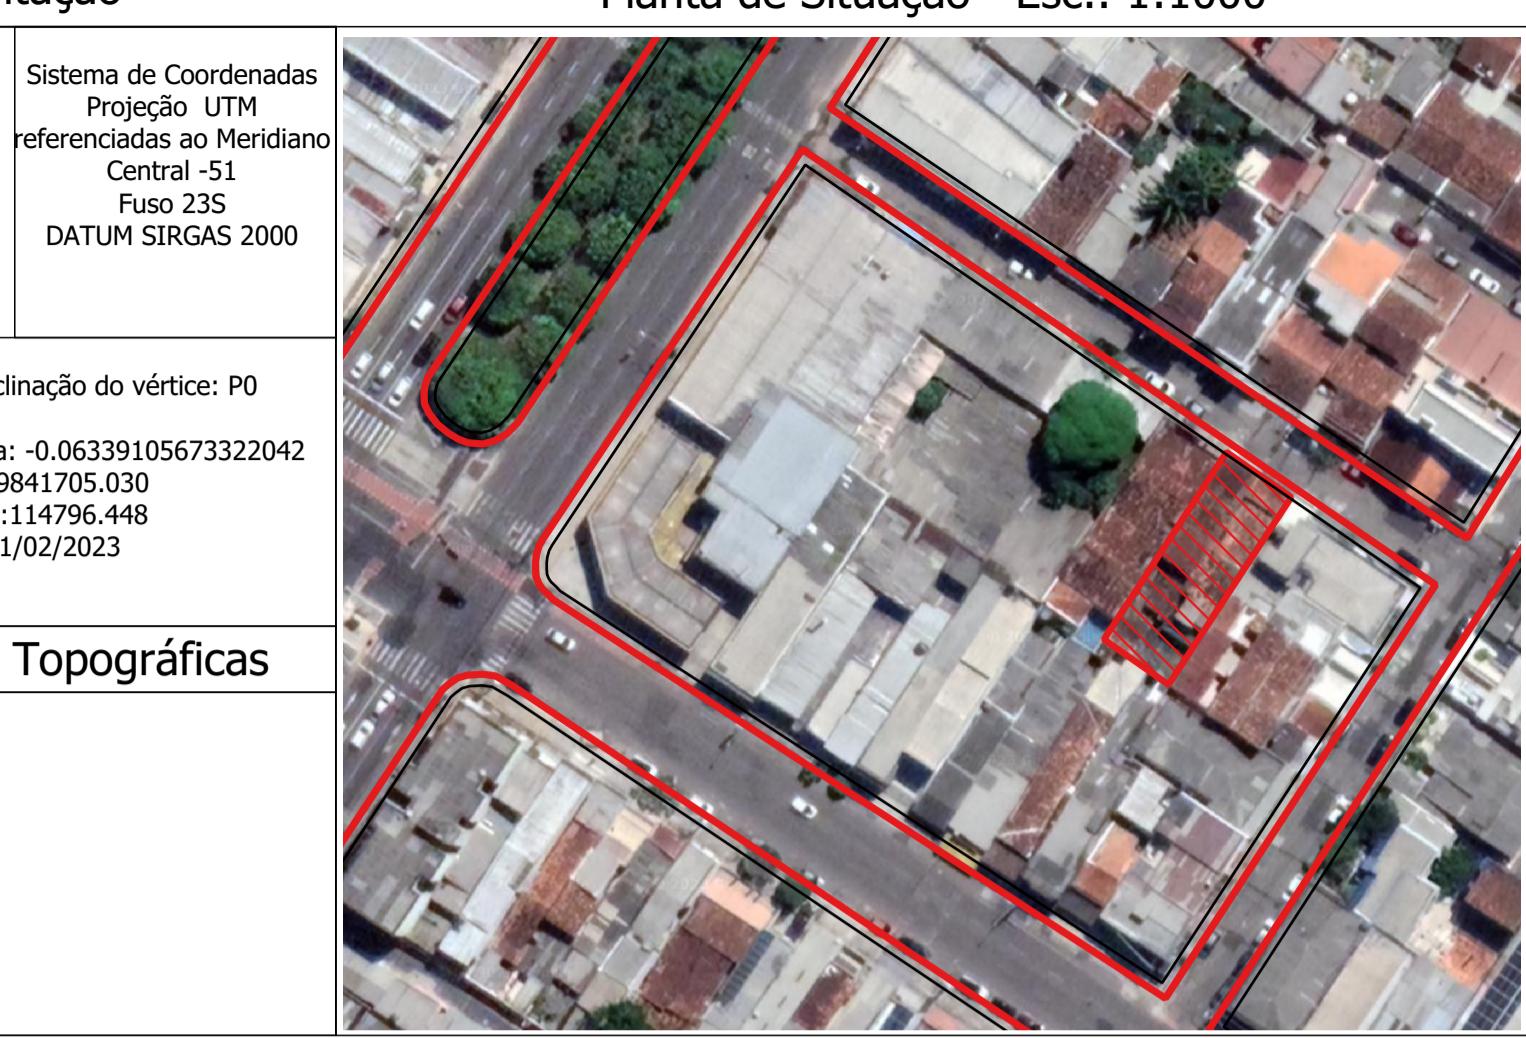

Planta de Situação - Esc.: 1:1000

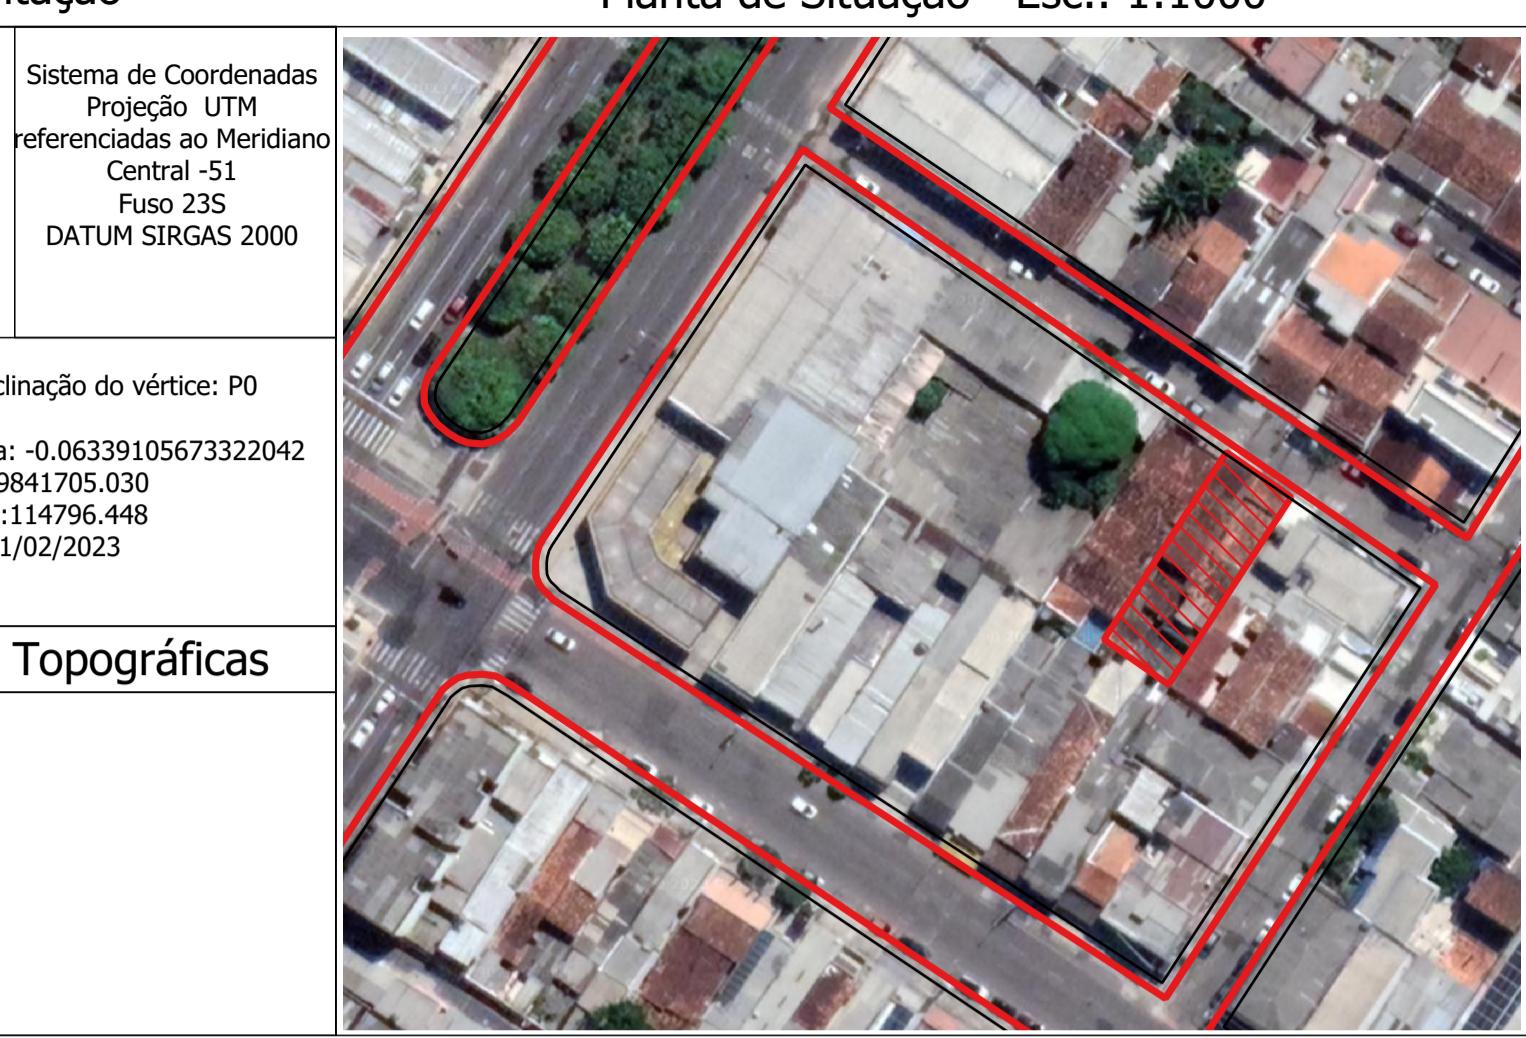

VÉRTICES VANTE, AZIMUTES, DISTÂNCIAS E COORDENADAS UTM DO IMÓVEL

Estação	Vante	Coordenada E	Coordenada N	Az Plano	Az Real	Distância
P0	P1	114796.4475	9841705.0296	124°40'22.46"	124°36'34.23"	10.00
P1	P2	114805.2227	9841698.0595	213°16'21.65"	213°12'33.43"	30.00
P2	P3	114788.6605	9841673.7198	304°38'15.71"	304°34'27.48"	10.00
P3	P0	114779.8835	9841679.7831	33°16'6.97"	33°12'18.74"	30.00

CONFINANTE À OESTE
OCUPANTE DO LOTE 36

CONFINANTE À LESTE
OCUPANTE DO LOTE 34

CONFINANTE À LESTE
OCUPANTE DO LOTE 33


CONFINANTE À LESTE
OCUPANTE DO LOTE 32

CONFINANTE AO SUL
OCUPANTE DE TV. LOMAS VALENTINAS, NÚMERO 1703

CONFINANTE AO SUL
OCUPANTE DE TV. LOMAS VALENTINAS, NÚMERO 1709



Título:	PLANTA DO TERRENO GEOREFERENCIADO		Folha:
LOTE TOTAL			01/03
Imóvel:	Lotes 14 e 20 da Passagem Grão Pará	Matr./ Transcrição	Cartório:
End.:	Passagem Grão Pará, número 14, Marco	Código:	Circunscrição:
Município:	BELÉM	Estado:	PARÁ
Área do Terreno:	300 m ²	Perímetro do Terreno:	80,00 m
Carimbo:		Proprietário:	
		MARIA LUIZA DA SILVA COSTA CPF : 080.510.032-00	
		Resp. Técnico:	
		ENG. CIVIL PABLO MARQUES CREA/PA: 1514262584 BR-316, Km 05, 5700, ANANINDEUA/PA	
Aprovações	ART N°	ART (PLANTA) N°	ART (MEMORIAL) N°

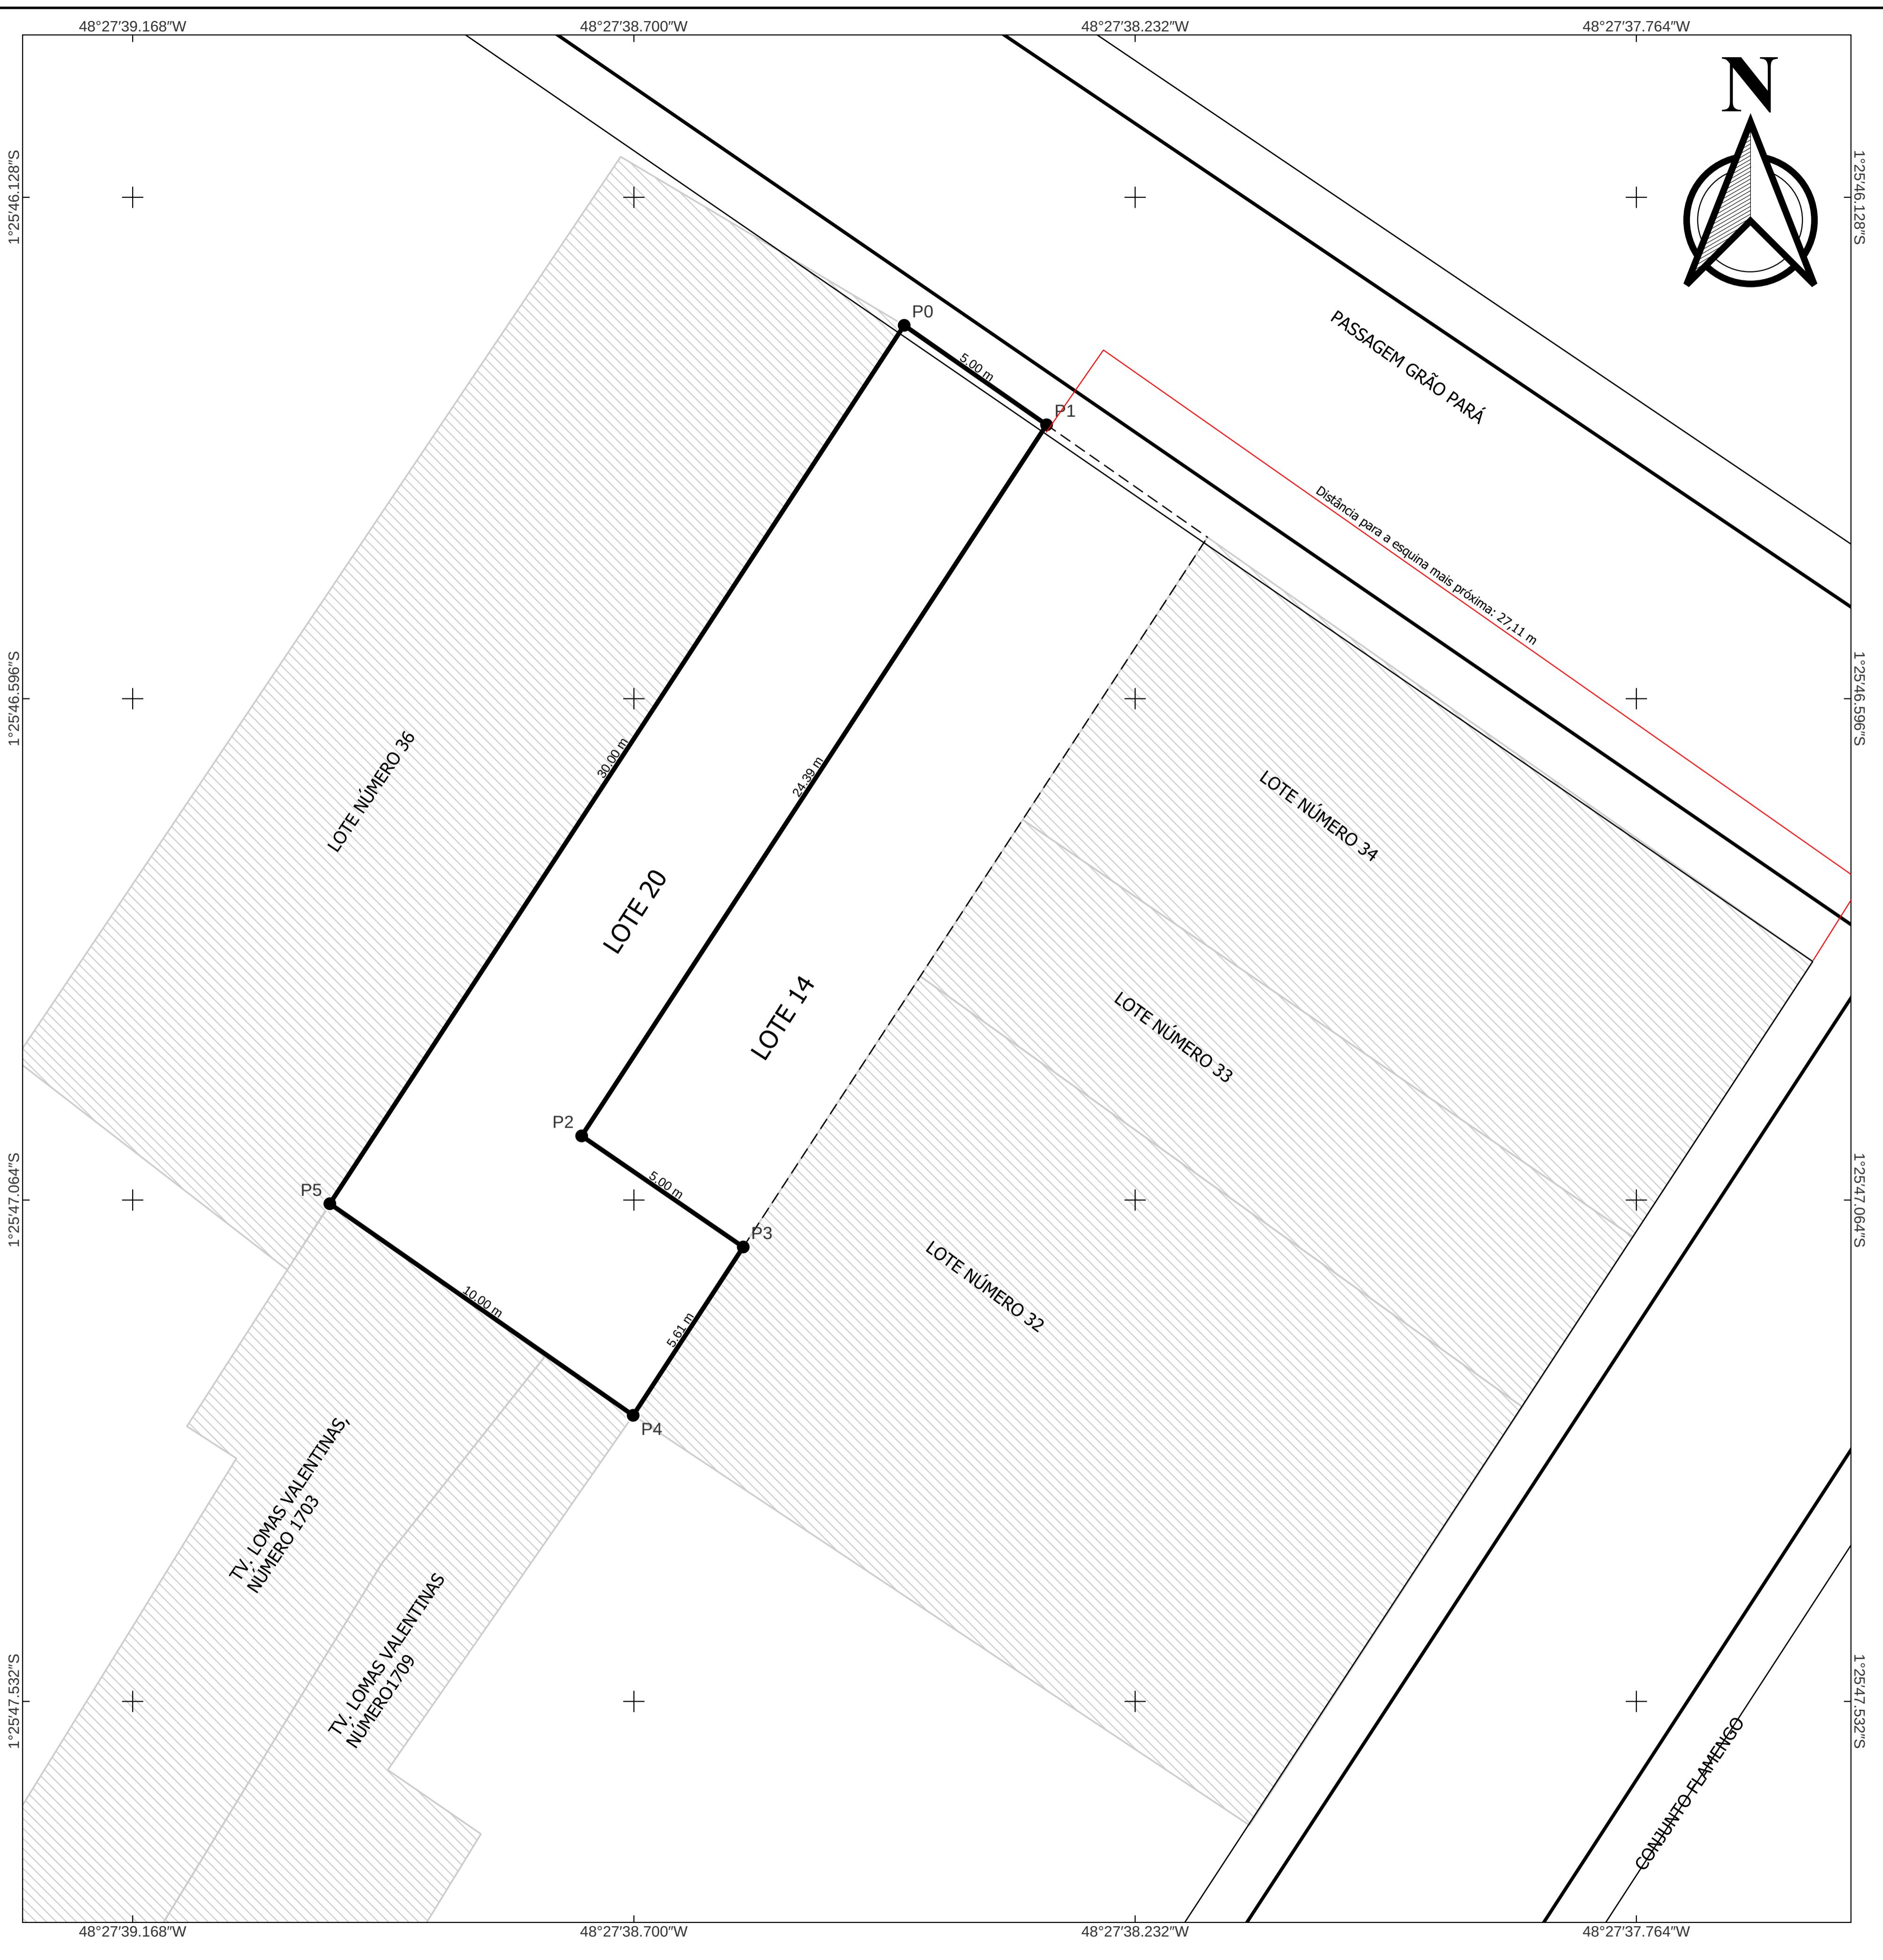

MOKEDO
ENGENHARIA DE SEGURANÇA DO TRABALHO E CONSTRUÇÃO CIVIL

**Título: PLANTA DO TERRENO GEORREFERENCIADO
IOTE A** Folha: **02/03**

Imóvel: Lote 20 da Passagem Grão Pará	Matr./ Transcrição: 008/34882/42/55/0232/000/000-44	Cartório:
End.: Passagem Grão Pará, número 20, Marco	Código:	Circunscrição:
Município: BELÉM	Estado: PARÁ	Comarca BELÉM
Área do Terreno: 179.00 m ²	Perímetro do Terreno: 81,00m	Escala: 1:100 Data: Ago./2023
Carimbo:	Proprietário: MARIA LUIZA DA SILVA COSTA CPF : 080.510.032-00	
	Resp. Técnico: ENG. CIVIL PABLO MARQUES CREA/PA: 1514262584 BR-316, Km 05, 5700, ANANINDEUA/PA	
Aprovações	ART Nº ART (PLANTA) Nº ART (MEMORIAL) Nº	

